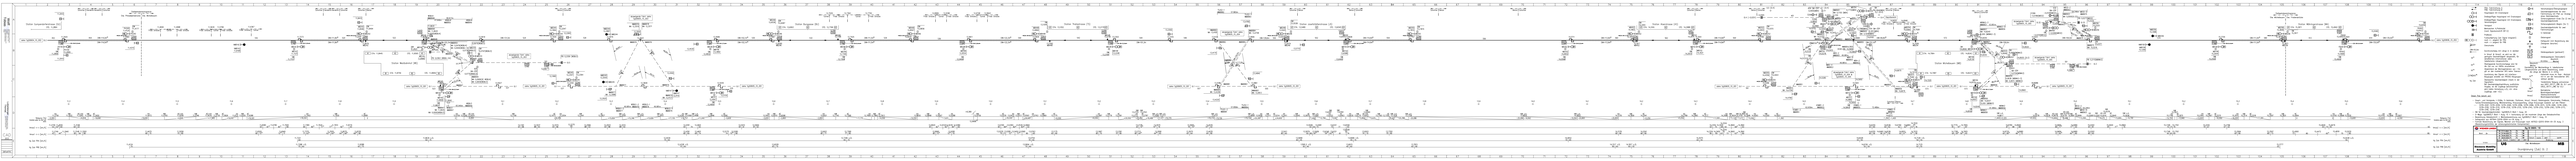

Wolff Tobias

Digital signiert von Wolff Tobias
DN: cn=Wolff Tobias, c=DE, o=Siemens, email=tobiaswolff@siemens.com
Datum: 2023.11.28 15:56:51 +01'00'

Loibelsberger Thomas

Digital signiert von Loibelsberger Thomas
DN: cn=Loibelsberger Thomas, o=Siemens, email=thomas.loibelsberger@siemens.com
Datum: 2023.11.17 11:30:20 +01'00'

CAD
2023

297x4715

Station Gumpendorferstrasse (GU)
STE: 11,2864
siehe SgSI0604_10_002
Gl.2
Stellwerksbereichsgrenze
Stw. Philadelphiabrücke | Stw. Michelbeuern
Schotter | Heraklith | Heraklith | Schotter
Freie Strecke | Tunnel | Freie Strecke
Station Westbahnhof (WS)
STA: 11,8445
STE: 11,9595
abzweigende Fahrt siehe SgSI0605_10_003
Station Burggasse (BU)
STA: 12,6063
STE: 12,7196
Station Thaliastrasse (TS)
STA: 13,1052
STE: 13,2170
abzweigende Fahrt siehe SgSI0605_10_004
Station Josefstädterstrasse (JS)
STA: 13,5480
STE: 13,6545
Station Alserstrasse (AS)
STA: 14,1916
STE: 14,2988
Station Michelbeuern (MB)
STA: 14,7064
STE: 14,8242
abzweigende Fahrt siehe SgSI0605_10_005
Stellwerksbereichsgrenze
Stw. Michelbeuern | Stw. Friedensbrücke
Station Währingerstrasse (WÄ)
STA: 15,3871
STE: 15,4942
siehe SgSI0606_10_002
siehe SgSI0605_10_001
Gl.1
Gl.2
Gl.3
Gl.4
Gl.5
Neigung [‰]
Vorzeichen gelten von links nach rechts
Vmax2 <-> [km/h]
Vmax1 <-> [km/h]
Vg Zub FRA [km/h]
Vg Zub FRB [km/h]

FRA: Fahrtrichtung A FRB: Fahrtrichtung B	
	Hauptsignal mit Ersatzsignal
	Dreibegriffiges Hauptsignal mit Ersatzsignal
	Dreibegriffiges Hauptsignal mit Ersatzsignal, Verschubsignal
	Vorsignal
A	Merkzeichen A/Haltetafel (nach Signalvorschrift §17.2)
☒	Prellbock
	Funkaufwertung (am Signal integriert) nach <- zeigend für FRA nach -> zeigend für FRB
XX,Xm	Grenzmarke
DW=XX,Xm	Durchrutschweg mit Länge in m darüber
XX*1	In Vmax1 & Vmax2: es wird nur die geringste Geschwindigkeit dargestellt, für detailliertere Informationen siehe tabellarische Längenschnitte
XX*2	Überlappende Durchrutschwege sind für die Zub nur zur Hälfte anzunehmen
XX*3	Abweichend der Montagetoleranz von −1m gilt an den markierten GKS keine Toleranz
[STW]XXX*6	Ausrüstung des Signals mit Interface-Baugruppe anstelle von PROSIG-Baugruppe
Vg Zub	Überwachte Geschwindigkeit (Vsoll) in der Signalfahrt. Bei Geschwindigkeitserhöhung zusätzliche Angabe, ob die Zuglänge berücksichtigt wird (siehe Anmerkung o.ZL, d.h. ohne Zuglänge, oder +ZL)

	Verschubsignal/Übergangssignal
V	Geschwindigkeitstafel für eine Fahrtrichtung mit Pfeil zur Anzeige eines Gleichswechsels
V	Sicherungsbereich-Ende (So 2) inkl. Geschwindigkeitstafel
	Sicherungsbereich-Beginn (So 1)
V1 V2	Geschwindigkeitstafel für zwei Fahrtrichtungen
	S-Verbinder
	Gleismagnet
HP-KM	Haltepunkt (mit Bezeichnung des Zielsignals darunter)
	I-Stoß
GKS-KM Nr.	Gleiskoppelspule (gesteuert)
GKS-KM Nr.	Gleiskoppelspule (festcodiert)
Abschnitt Weiche XX.XXXm Abschnitt Weiche	Darstellung der Weichenlänge lt. tabellarischer Längenschnitte und deren Bezeichnung, sowie die Länge der Weiche in m mittig
XX*4	Haltetafel muss im fixen Abstand 4,4 m von der festcodierten GKS verbaut werden
Neigung KM*5	Tatsächliche Neigung entnommen aus U6G1_161111_ZWG für Gl.1 und U6G2_161111_ZWG für Gl.2
Vmax1	Betriebliche Maximalgeschwindigkeit
Vmax2	Oberbautechnische Maximalgeschwindigkeit

Dieser Plan beruht auf:

- Haupt- und Vorsignale, I-Stöße, S-Verbinder, Stationen, Vmax1, Vmax2, Gleismagnete, Grenzmarke, Prellbock, Tunnel/Streckenbegrenzung, Weichenanfang, Kreuzungsanfang, Länge Kreuzungen basieren auf den Plänen:
  -- 5378-202F, 5378-203D, 5378-204D, 5378-205B, 5378-206B, 5378-207C, 5378-208C, 5378-209C, 5378-210D, 5378-211D, 5378-212E, 5378-213C, 5378-214C, 5378-215C, 5378-216C, 5378-217C, 5378-218C, 5378-219C
- KM für Geschwindigkeitstafeln: SgGi0605/2 Blatt 1 Ausg. 20
- D-Wege: SgGi0605/1 Blatt 1 Ausg. 10 + Aufrundung auf die maximale Länge des Gleisabschnittes
- Bezeichnung Gleisabschnitt + Weichenbezeichnung aus SgGi0605/1 Blatt 1 Ausg. 10
- Haltepunkte aus A97944-S2016-B164-xx-C6 Ausg. 3
- Formale Bezeichnung der Signale, Weichen und Kreuzungen nach A97922-Q2010-B164-XX-35 Ausg. 3 (Bezeichnungsrichtlinie der sicherungstechnischen Komponenten)

WIENER LINIEN

Sg Sl 0605 / 10

Blatt 2+

Ausg.	Datum	bearb.	gez.	gepr.	Datum	bearb.	gepr.	betrifft
04	17.11.2023	TL	TL	TW				
03	27.04.2023	TL	TL	TW				
02	19.04.2023	TL	TL	TW				
01	29.03.2023	TL	TL	TW				

Änderung

TLP:GELB

Siemens Mobility Austria GmbH

U6

Stw. Michelbeuern

MB

Grundplanung (Zub) Gl. 2